



CONCEPT, NOT FOR FABRICATION

CoolShade · github.com/BoujeeEnjinia1701/coolshade

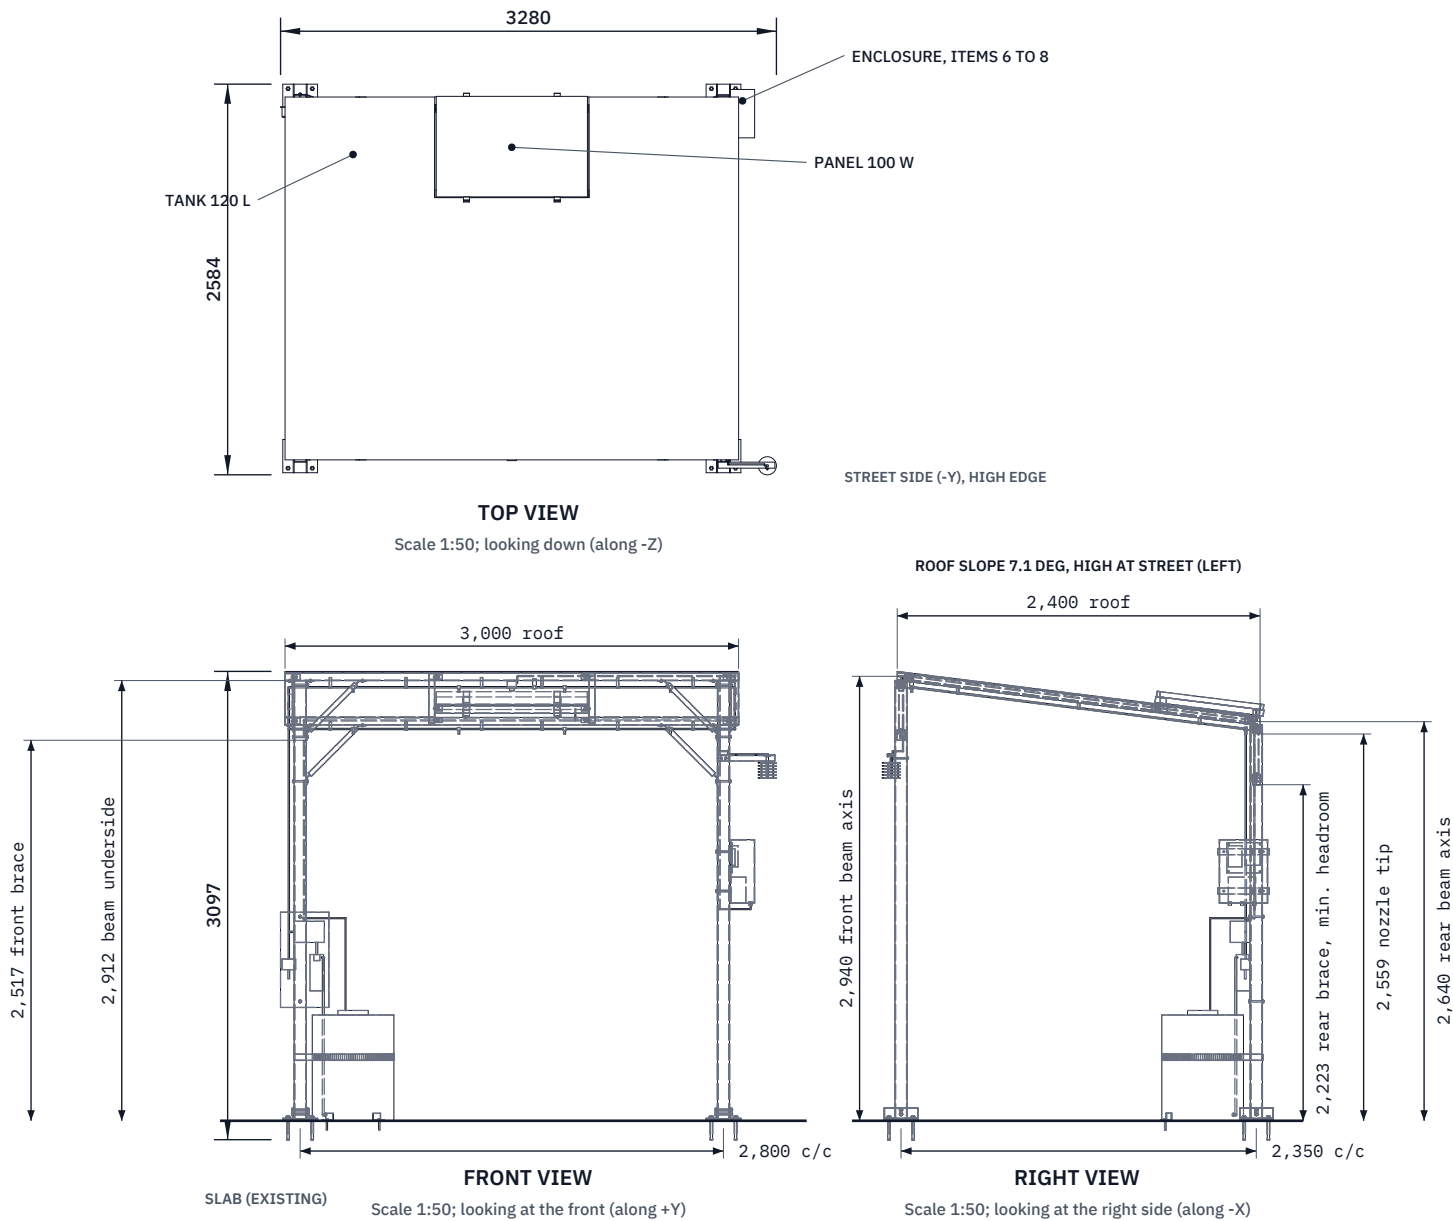

REV	DESCRIPTION	DATE	BY
P1	Preliminary GA for TRL 3 (from cad/src/model.py)	2026-09-25	AC
P2	Recommendations accepted (DDR-002): 25 Ah battery, R10 wind notes	2026-09-25	AC
P3	Layout and labels tidied	2026-09-25	AC
P4	Constructable design (CSH-DDR-003): 2,350 post grid, cleats, panel at rear	2026-09-30	AC

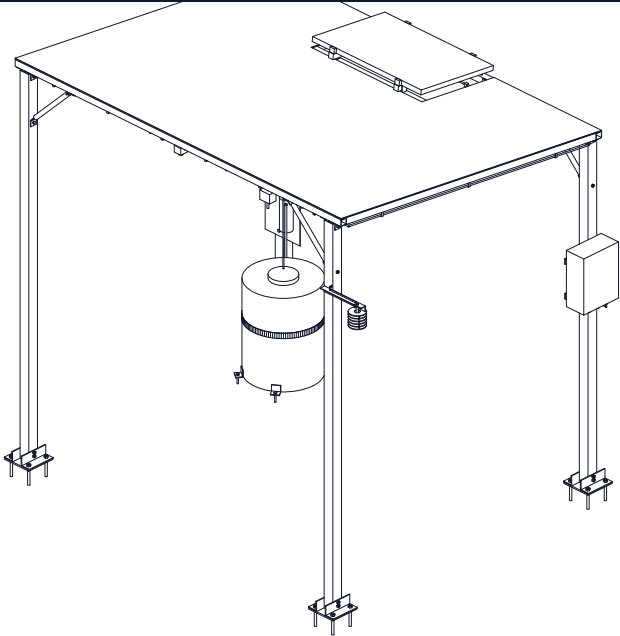

ISOMETRIC VIEW

Not to scale; seen from the front right and above, about 30 deg elevation

MAIN DIMENSIONS AND INTERFACES (MM)

Roof 3,000 x 2,400 (7.2 m2), mono-pitch 7.1 deg, high at the street
Posts 80 x 80 x 3 SHS on 2,800 x 2,350; beams 50 x 2 SHS
Knee braces 32 OD, flattened ends; bends 350 down, 350 along; headroom 2,223 min.
Base plates 220 sq. x 10 with 2 angle cleats; 4 x M16 at 160; about 2.8 kN factored
Roof joints: 50 x 50 x 5 angle cleats, M8 bolts into rivet nuts; no welding
Mist loop 11.9 m, 6.5 bore, 8 nozzles 0.4 mm; vacuum breaker at front
Tank 120 L, strapped to the rear left post; drain valve at the low point
Enclosure 160 x 320 x 420 on rails, rear right post, 1,440 to 1,860; 25 Ah
Panel at the rear edge on a bearer and L-feet; pump on a plate, rear left post
Fabric fitted only in forecast gusts below 15 m/s; frame checked fabric-off at 30 m/s (CSH-CAL-001)
Third-angle; front view from the street (-Y); slab by others, checked per site

COOLSHADE

github.com/BoujeeEnjinia1701/coolshade

General arrangement

DRAWING NO. CSH-DWG-001		REV P4	SHEET 1 of 1	SIZE ANSI B
SCALE 1:50	UNITS mm	PROJECTION 	DATE 2026-09-30	DRAWN Amish Chadha
MATERIAL / NOTES Galvanized S275 SHS frame; bought-in parts per bom/bom.csv. PRELIMINARY, NOT FOR FABRICATION				
Licensed CERN-OHL-S-2.0 · Design Molecule Lab · designmolecule.com			Generated from cad/src; do not edit by hand	