
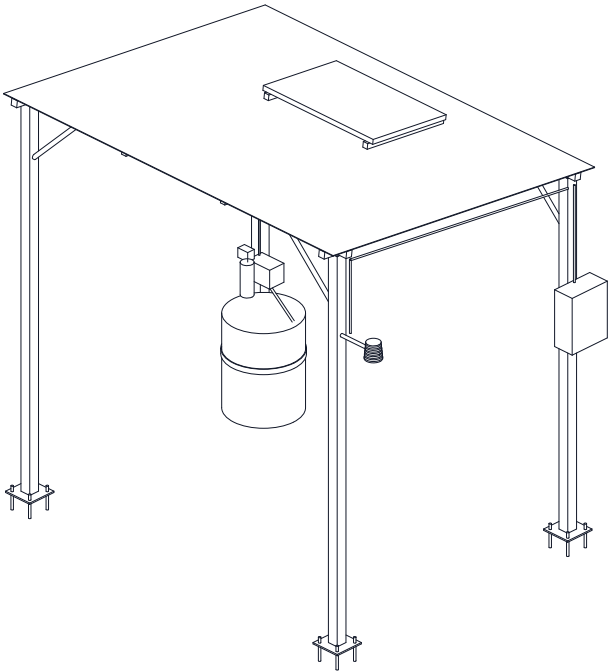


CONCEPT, NOT FOR FABRICATION

REV	DESCRIPTION	DATE	BY
P1	Preliminary GA for TRL 3 (from cad/src/model.py)	2026-09-25	AC

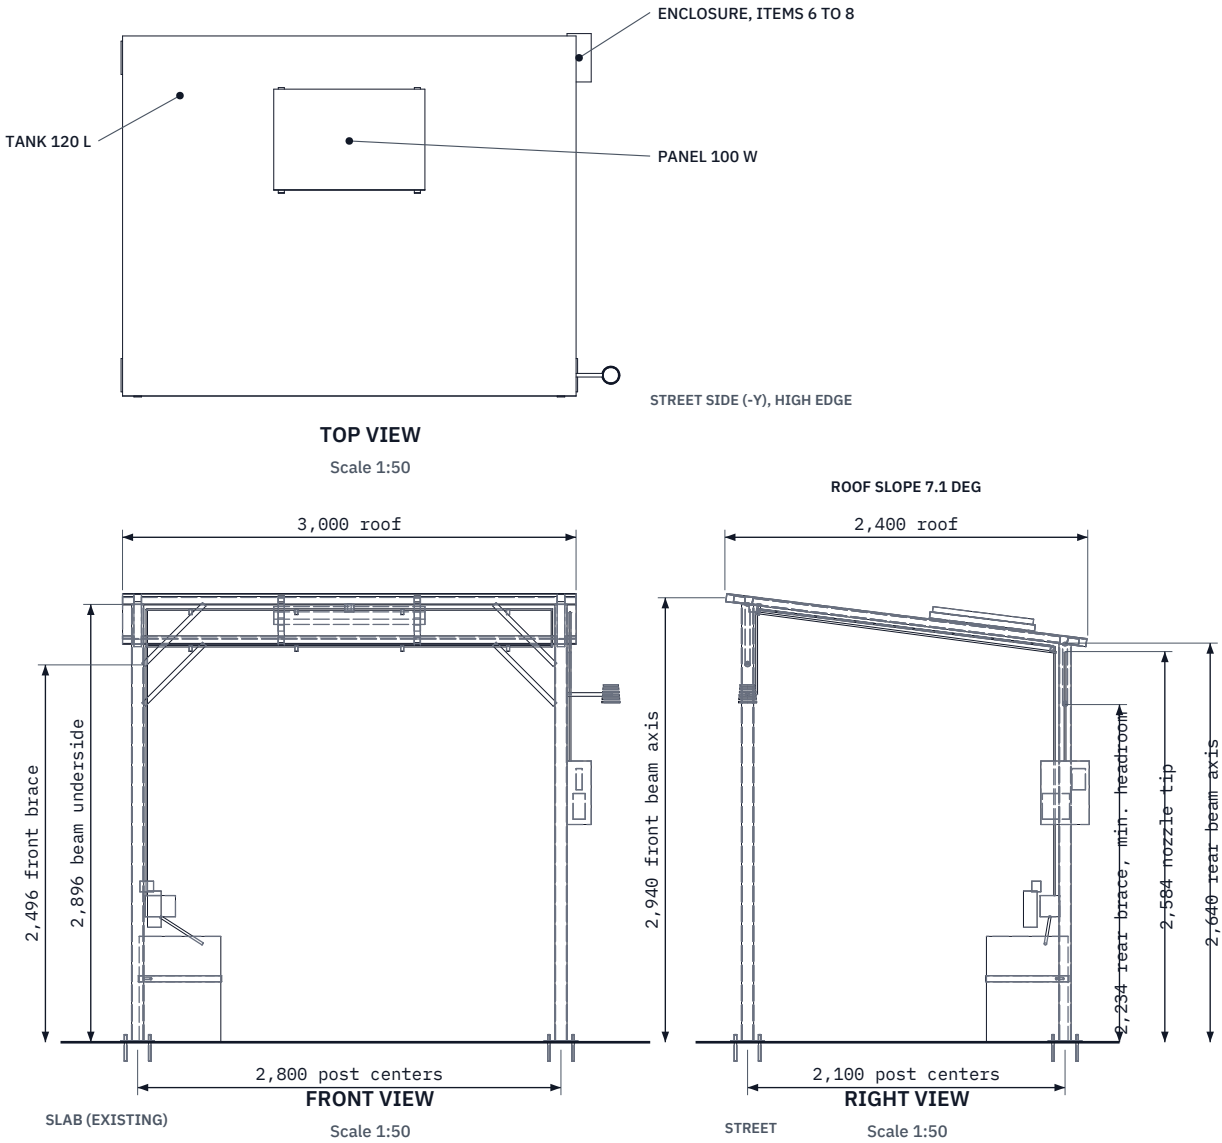

ISOMETRIC VIEW
Not to scale

MAIN DIMENSIONS AND INTERFACES (MM)

Roof 3,000 x 2,400 (7.2 m2), mono-pitch 7.1 deg, high at the street
Posts 80 x 80 x 3 SHS on 2,800 x 2,100; beams 50 x 2 SHS
Knee braces 32 OD, 400 down x 400 along; headroom 2,234 min.
Base plates 220 x 220 x 10, 4 x M16 at 160; anchors about 6.4 kN factored
Mist loop 11.0 m, 6.5 bore, 8 nozzles 0.4 mm; vacuum breaker at front
Tank 120 L, strapped to the rear left post; drain valve at the low point
Enclosure 160 x 320 x 420 on the rear right post, 1,440 to 1,860
Fabric off before storms: beams overloaded with fabric above about 16 m/s (CSH-CAL-001)
Third-angle; front view from the street (-Y); slab by others, checked per site

COOLSHADE

General arrangement

DRAWING NO. CSH-DWG-001			REV P1	SHEET 1 of 1	SIZE ANSI B
SCALE 1:50	UNITS mm	PROJECTION 	DATE 2026-09-25		DRAWN Amish Chadha
MATERIAL / NOTES Galvanized S275 SHS frame; bought-in parts per bom/bom.csv. PRELIMINARY, NOT FOR FABRICATION					
Licensed CERN-OHL-S-2.0 · Open Hardware Portfolio · amishchadha.com			Generated from cad/src; do not edit by hand		