



CONCEPT, NOT FOR FABRICATION


REV	DESCRIPTION	DATE	BY
P1	Concept sheet	2026-09-25	AC

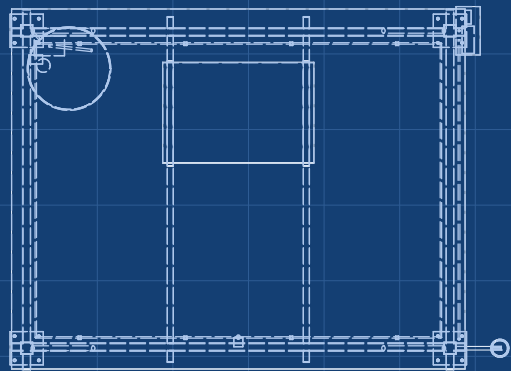


TOP VIEW
Scale 1:50

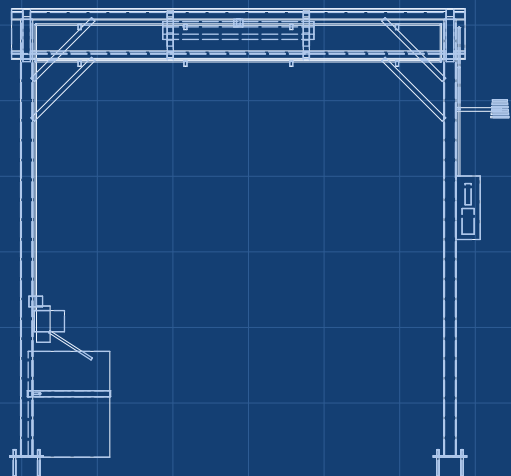

FRONT VIEW
Scale 1:50

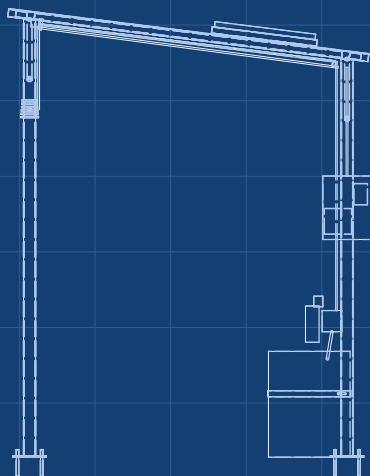

RIGHT VIEW
Scale 1:50

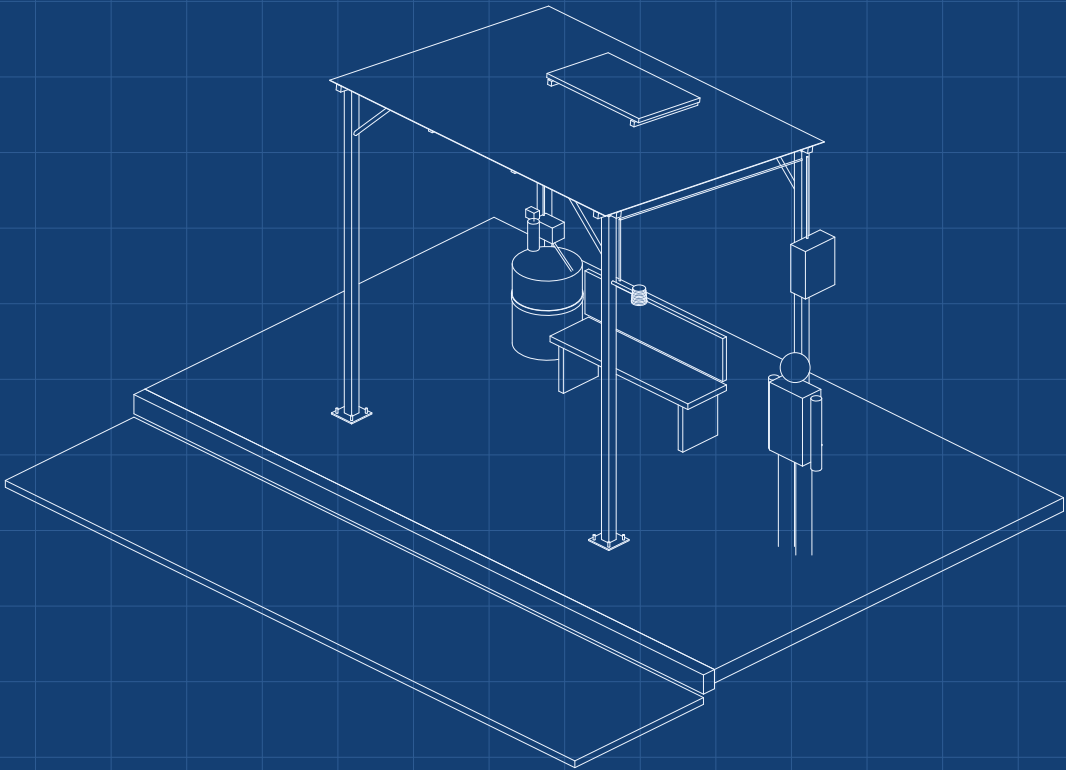

ISOMETRIC VIEW
Not to scale; figure is a 1.75 m person

KEY FIGURES

Shade roof 3.0 x 2.4 m (7.2 m²); headroom 2,234 mm minimum (CSH-CAL-001)
8 low-pressure nozzles at 7 bar, 32 L/h while spraying (nozzle data to confirm)
85 L water and 204 Wh per hot, dry day; 1.35 °C air cooling at 1 m/s
100 W panel, 12.8 V 20 Ah LiFePO4; 12 V DC only, no mains
Mists only above 32 °C, below 60 % RH, with people present
Fabric off before storms; \$758 in parts (indicative), \$700 budget

COOLSHADE

Solar misting shade canopy concept

DRAWING NO. CSH-DWG-010			REV P1	SHEET 1 of 1	SIZE ANSI B
SCALE 1:50	UNITS mm	PROJECTION 	DATE 2026-09-25	DRAWN Amish Chadha	

MATERIAL / NOTES
Massing model for concept communication