


CONCEPT, NOT FOR FABRICATION


CoolShade · github.com/BoujeeEnjinia1701/coolshade

REV	DESCRIPTION	DATE	BY
P1	Preliminary GA for TRL 3 (from cad/src/model.py)	2026-09-25	AC
P2	Recommendations accepted (DDR-002): 25 Ah battery, R10 wind notes	2026-09-25	AC

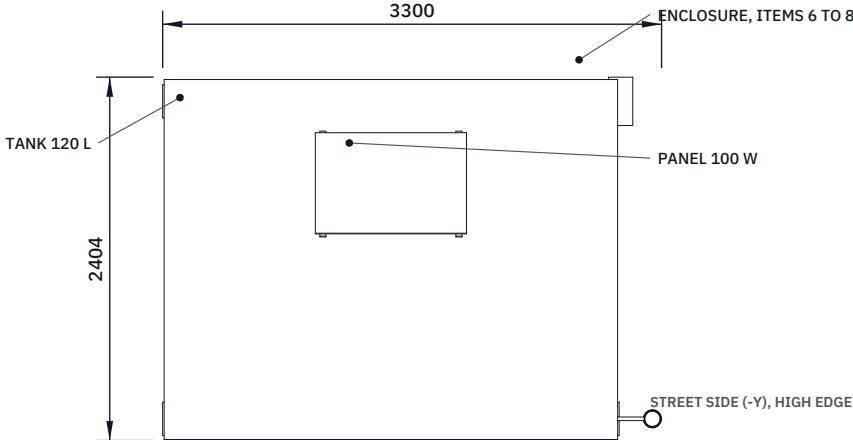


TOP VIEW

Scale 1:50; looking down (along -z)
3,000 roof

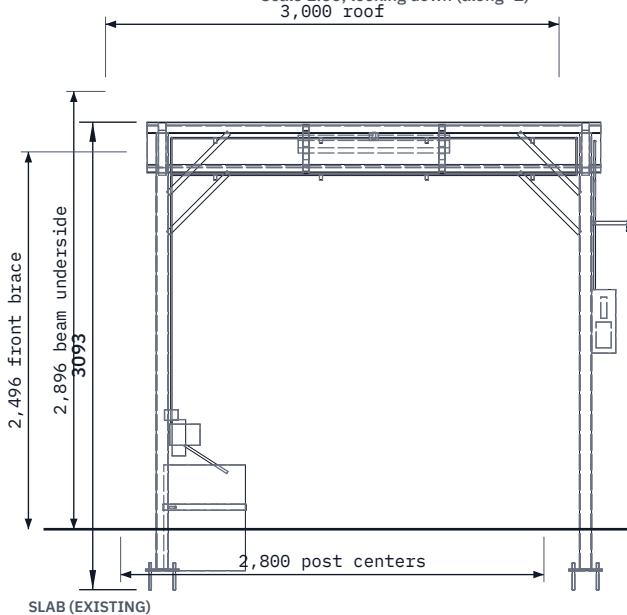


FRONT VIEW

Scale 1:50; looking at the front (along +Y)

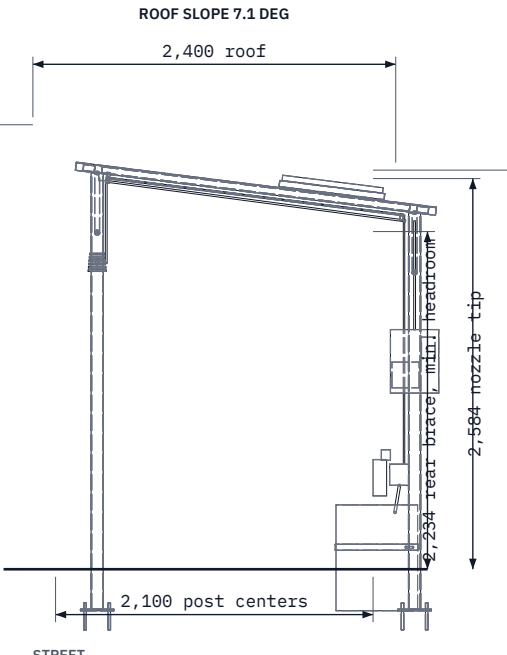

RIGHT VIEW

Scale 1:50; looking at the right side (along -X)

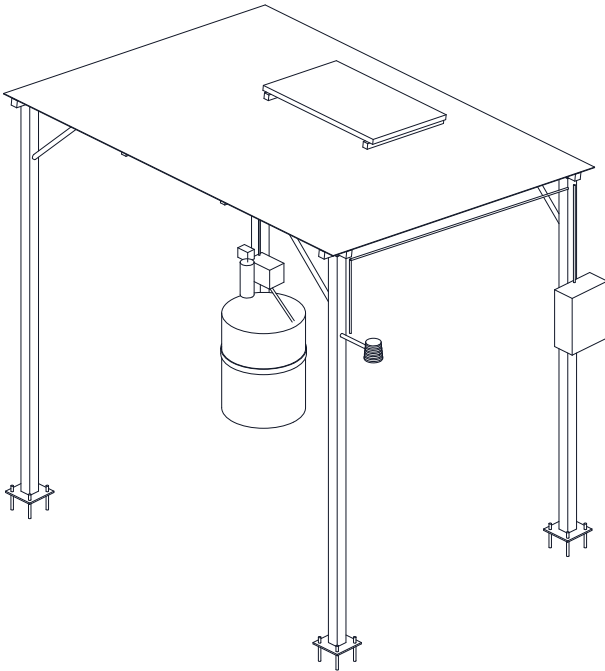

ISOMETRIC VIEW

Not to scale; seen from the front right and above, about 30 deg elevation

MAIN DIMENSIONS AND INTERFACES (MM)

Roof 3,000 x 2,400 (7.2 m²), mono-pitch 7.1 deg, high at the street

Posts 80 x 80 x 3 SHS on 2.800 x 2.100: beams 50 x 2 SHS

Knee braces 32 OD, 400 down x 400 along: headroom 2.234 min

Base plates 220 x 220 x 10, 4 x M16 at 160: anchors about 2.8 kN factored

Mist loop 11.0 m, 6.5 bore, 8 nozzles 0.4 mm: vacuum breaker at front

Tank 120 L, strapped to the rear left post; drain valve at the low point

Enclosure 160 x 320 x 420 on the rear right post, 1,440 to 1,860; battery 25 Ah

Fabric fitted only in forecast gusts below 15 m/s: frame checked fabric-off at 30 m/s (CSH-CAL-001)

Third-angle; front view from the street (-Y); slab by others, checked per site

COOLSHADE

github.com/BoujeeEnjinia1701/coolshade

General arrangement

DRAWING NO. CSH-DWG-001		REV P2	SHEET 1 of 1	SIZE ANSI B
SCALE 1:50	UNITS mm	PROJECTION 	DATE 2026-09-25	DRAWN Amish Chadha
MATERIAL / NOTES Galvanized S275 SHS frame; bought-in parts per bom/bom.csv. PRELIMINARY, NOT FOR FABRICATION				

Licensed CERN-OHL-S-2.0 · Design Molecule Lab · designmolecule.com

Generated from cad/src; do not edit by hand